


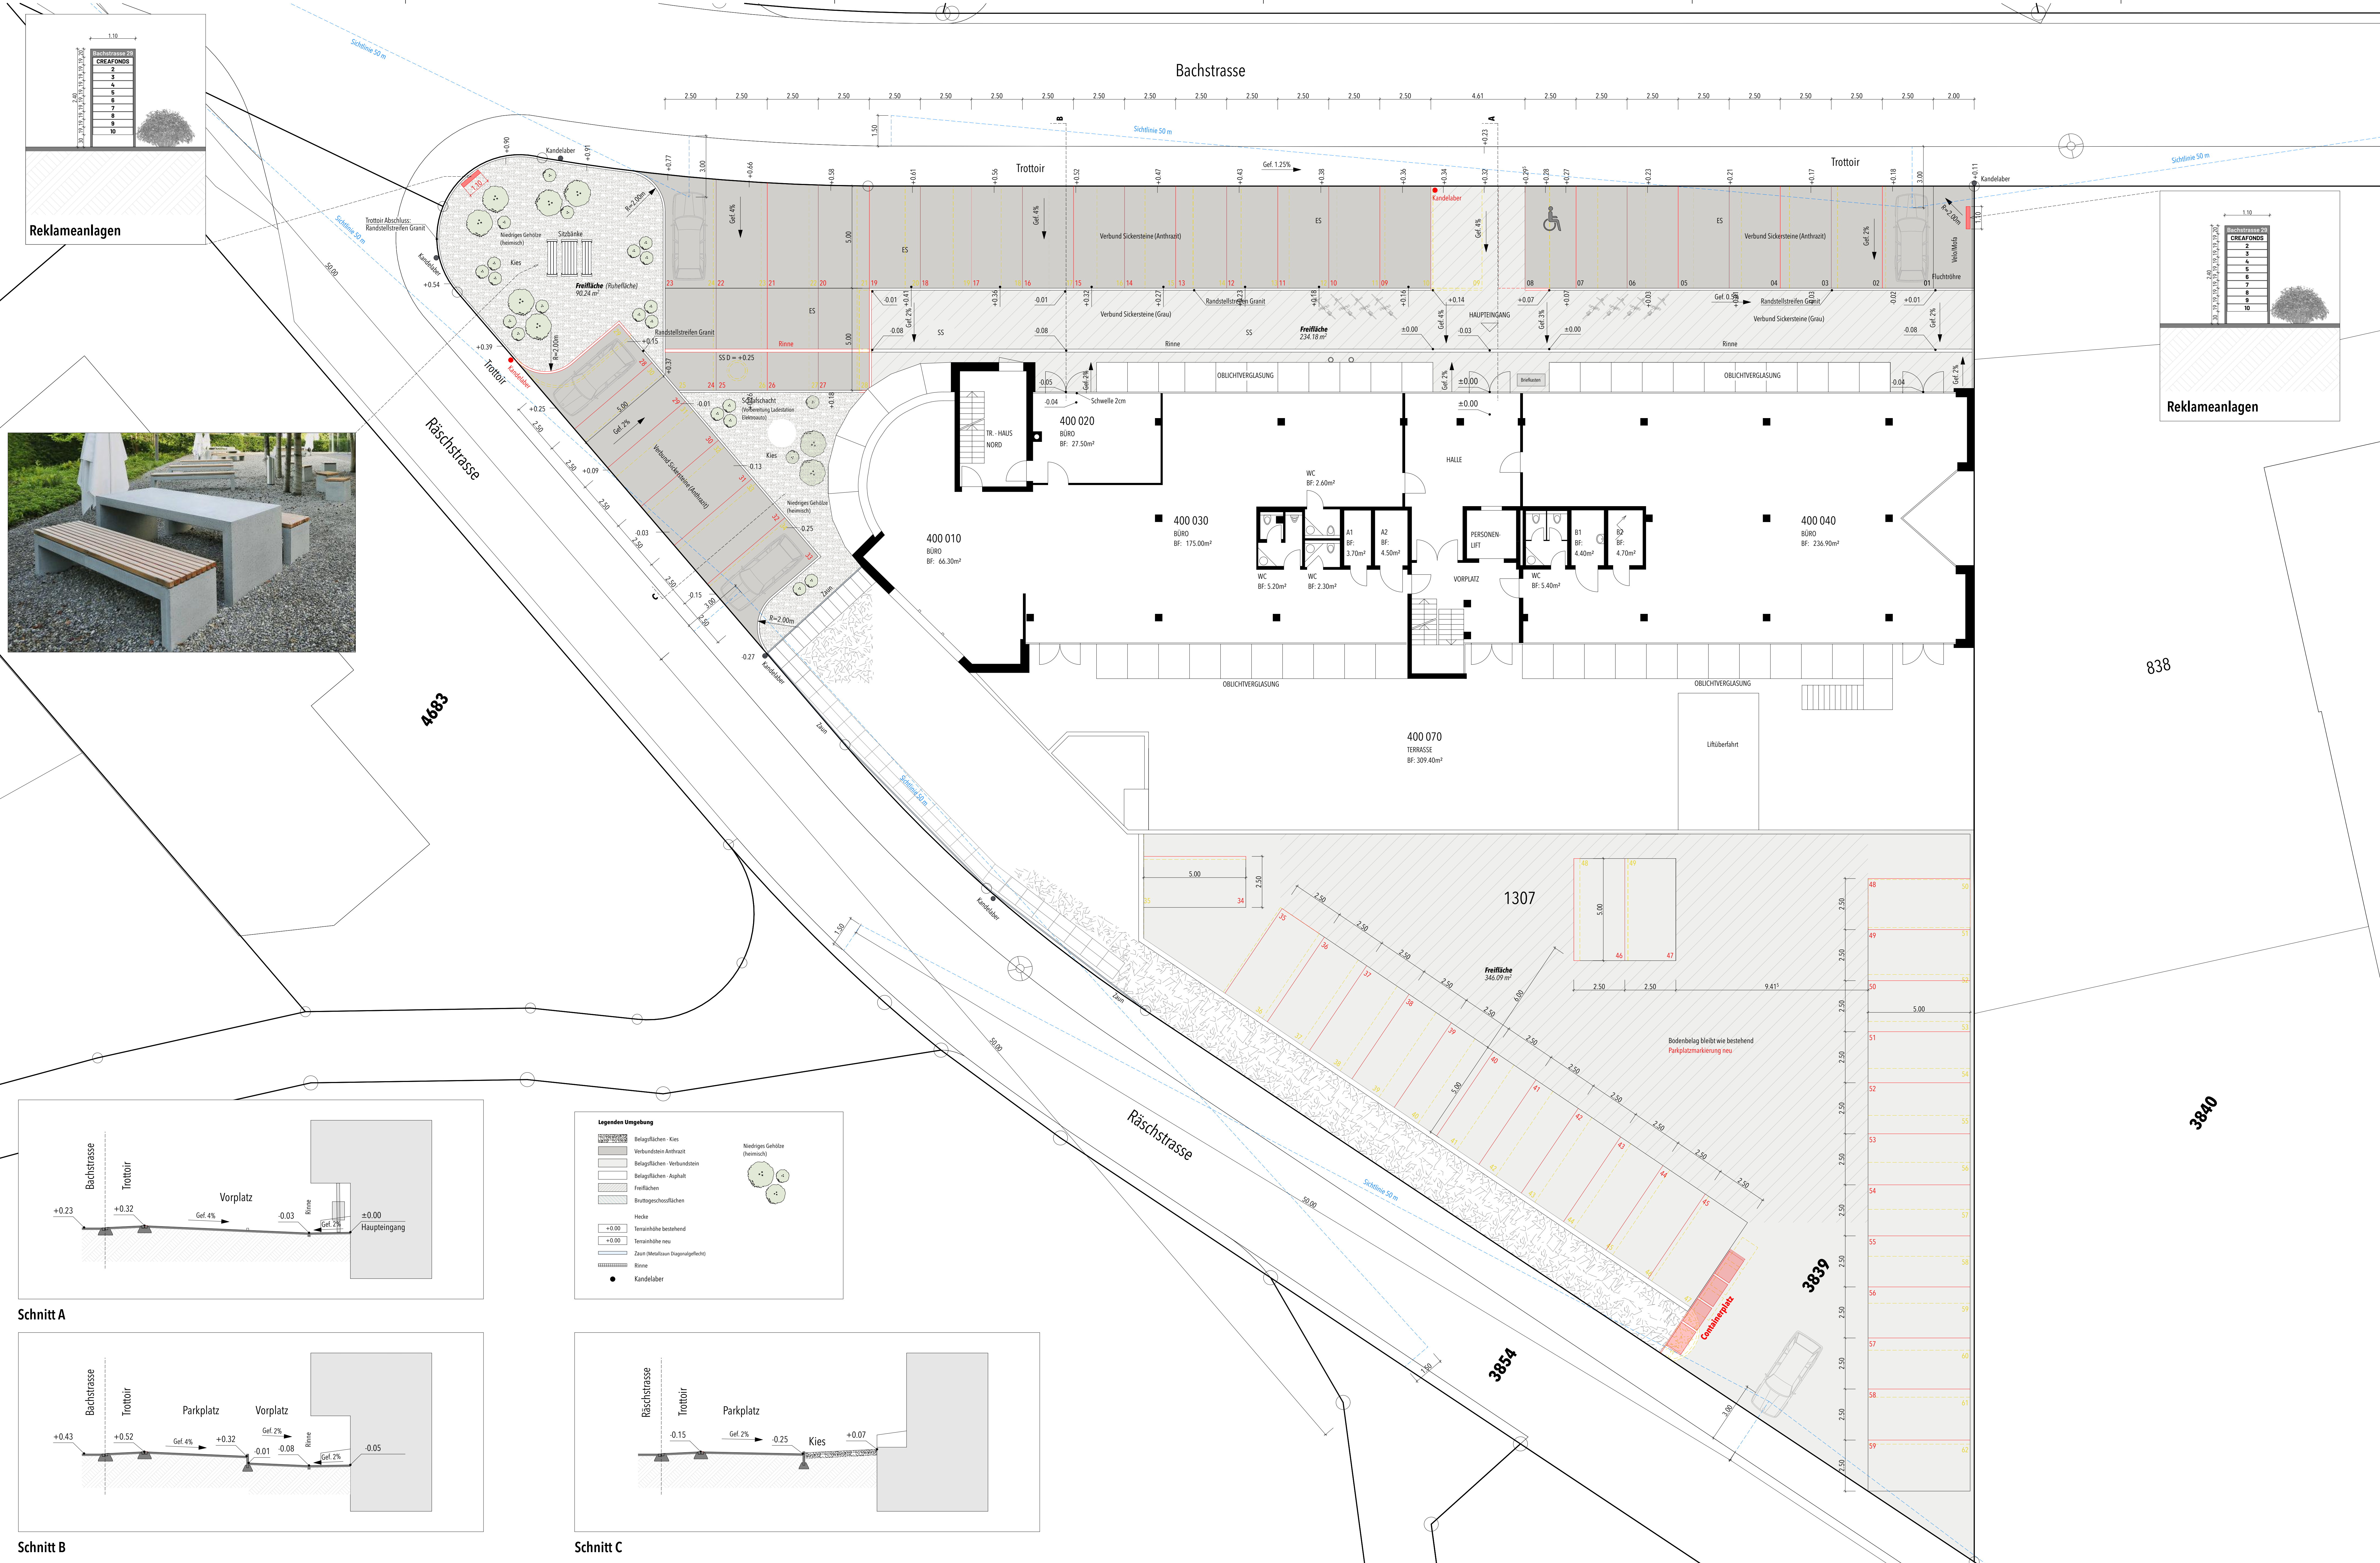

PROJEKT

Parkplatzerweiterung

Creafonds AG
Bachstrasse 29
8912 Obfelden

125

PLAN NR.	32.3	MASSSTAB	1:100	GRÖSSE	84/60	KLUSSTER	3839
PROJEKT	Rev. BAUEINGABE						
LEGEND	BEISTAND ABBRUCH NEU						
REFERENZ	± 0.00 Eingang EG						

DATUM	09.11.20	GEZ.	AA	REVISIONSTEXT	
INDEX	23.11.20	AA			

ARCHITECTUR

BAUHERSCHAFT

Creafonds AG
Industriestrasse 5b
6210 Sursee LU

ATELIER AA
Architekten ETH
Chileweg 23 · CH-8912 Obfelden
www.atelier-aa.ch · +41 44 761 03 77

ARCHITECTUR

BAUHERSCHAFT

ATELIER AA
ARCHITECTEN ETH

Ort, Datum:

Obfelden, 09.11.2020

Bauherrschaft / Grundeigentümer:

Projektverfasser:

A. Hilt